SQD CHK

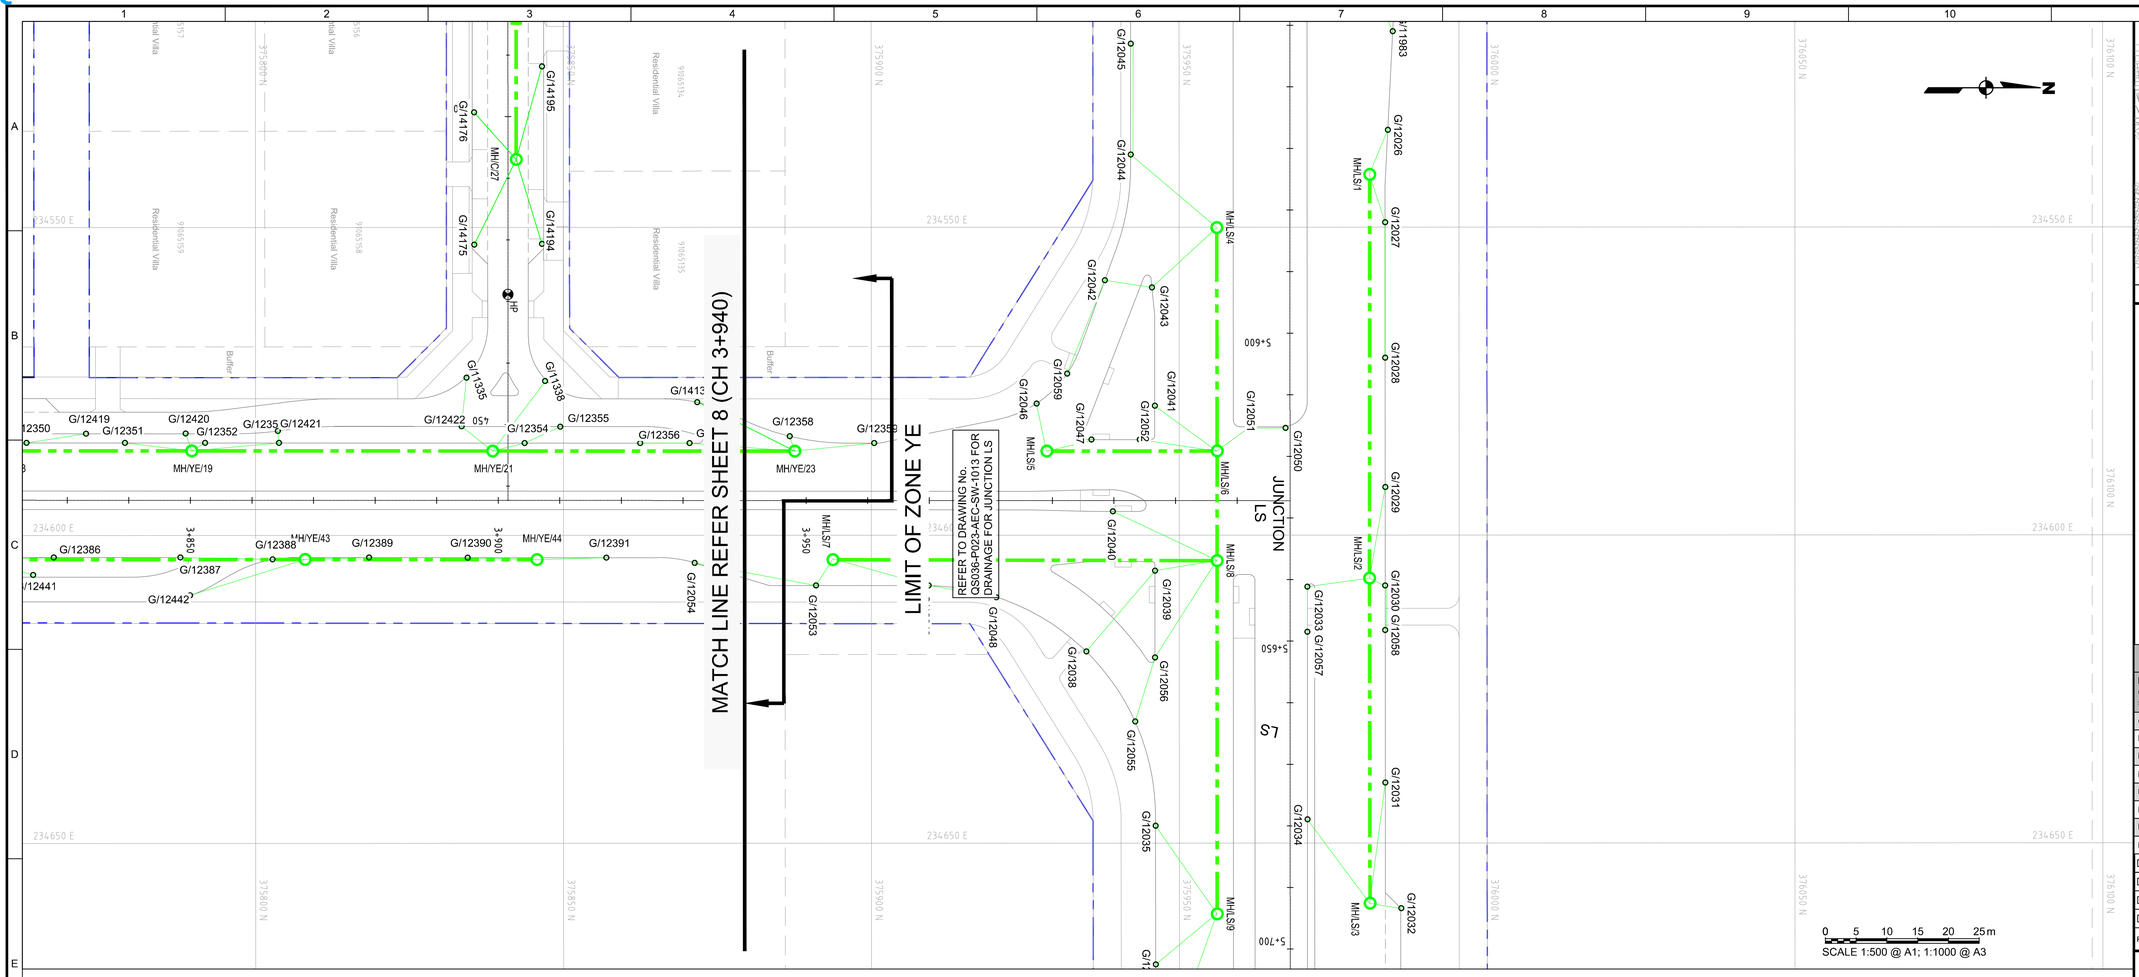

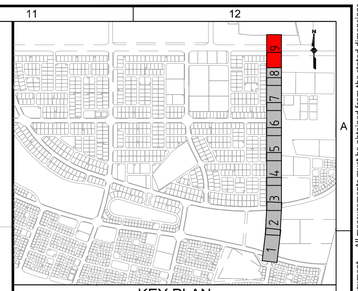

KEY PLAN

NOTES:

1. ALL DIMENSIONS ARE IN METRES UNLESS NOTED OTHERWISE.
2. ALL LEVELS ARE IN METRES AND RELATED TO QATAR NATIONAL DATUM 1995 (QND95).
3. ALL CO-ORDINATES ARE TO QATAR NATIONAL GRID
4. FOR ADDITIONAL NOTES AND PLAN LEGEND REFER TO DRAWING QS036-P00-AEC-SW-0999
5. DRAWINGS ARE TO BE READ IN CONJUNCTION WITH STANDARD DETAILS DRAWING QS036 - P00 - AEC - SW - 7100 - 7112
6. DRAWINGS ARE TO BE READ IN CONJUNCTION WITH PROFILE DRAWING - QS036 - P36 - AEC - SW - 2001 - 2014
7. DRAWINGS TO BE READ IN CONJUNCTION WITH MANHOLE SCHEDULES QS036-P00-AEC-SW-1600 SERIES AND GULLY SCHEDULES QS036-P00-AEC-SW-1500 SERIES.

SAFETY, HEALTH AND ENVIRONMENTAL INFORMATION

In addition to the hazards/risks normally associated with the types of work detailed on this drawing, note the following specific residual risks (Reference shall also be made to the design hazard log).

Construction
For Hazards Refer to Drawing No QS036-P00-AEC-HW-0997
Maintenance / Cleaning
None
Use
None
Decommissioning / Demolition
None

Rev.	Date	Revision Details	Drawn	Chkd.	Appd.
D04	24AUG17	REVISED DUE TO ROAD WIDENING	AK	JQ	WV
D03	30APR17	ISSUED FOR APPROVAL	AG	JQ	WV
D02	19DEC16	ISSUED FOR APPROVAL	AL	AT	WV
D01	31JUL15	REVISED AS PER DRC	AL	AT	AB

هيئة الأشغال العامة
Public Works Authority

P.O.Box: 22188
Tel.: 00974 44950000
Fax: 00974 44950999

قطر تستحق الأفضل
Qatar Deserves The Best
www.ashghal.gov.qa

IA

Checking and Verification

		Name	Signature	Date
Self-Check / Originator		K.S.V		
Checking	Checker	R.H		
Inter- disciplinary	HWY ENG			
	HWY CAD			
	WET ENG			
	WET CAD	J.M		
	DRY ENG			
	DRY CAD			
	STR ENG			
	STR CAD			
	Verifier	S.M		
	Approver	M.A		

Project Code: QS036

Status: DETAILED DESIGN

Drawing Title:

SURFACE & GROUNDWATER SYSTEM LAYOUTS ROAD MY00 (DRAINAGE YE)

Drawn:	A.LEWIS	Checked:	A.TAYLOR
Designed:	L.WASIEWICZ	Approved:	W.VANSTRAATE
Date:	JULY 2015	Scale:	AS SHOWN

Drawing Number: QS036-P36-AEC-SW-1009

Revision: D04

This drawing has been prepared for the use of AECOM's client. It may not be used, modified, reproduced or relied upon by third parties, except as agreed by AECOM or as required by law. AECOM accepts no responsibility, and denies any liability whatsoever, to any party that uses or relies on this drawing without AECOM's express written consent. Do not scale this document. All measurements must be obtained from the stated dimensions.

Plot Date: 18/10/2017 01:59:43 Login: johnson, Anju File Name: C:\pwworking\aecom ds04 eu\johnsona\dms39131\QS036-P36-AEC-SW-1009.dwg